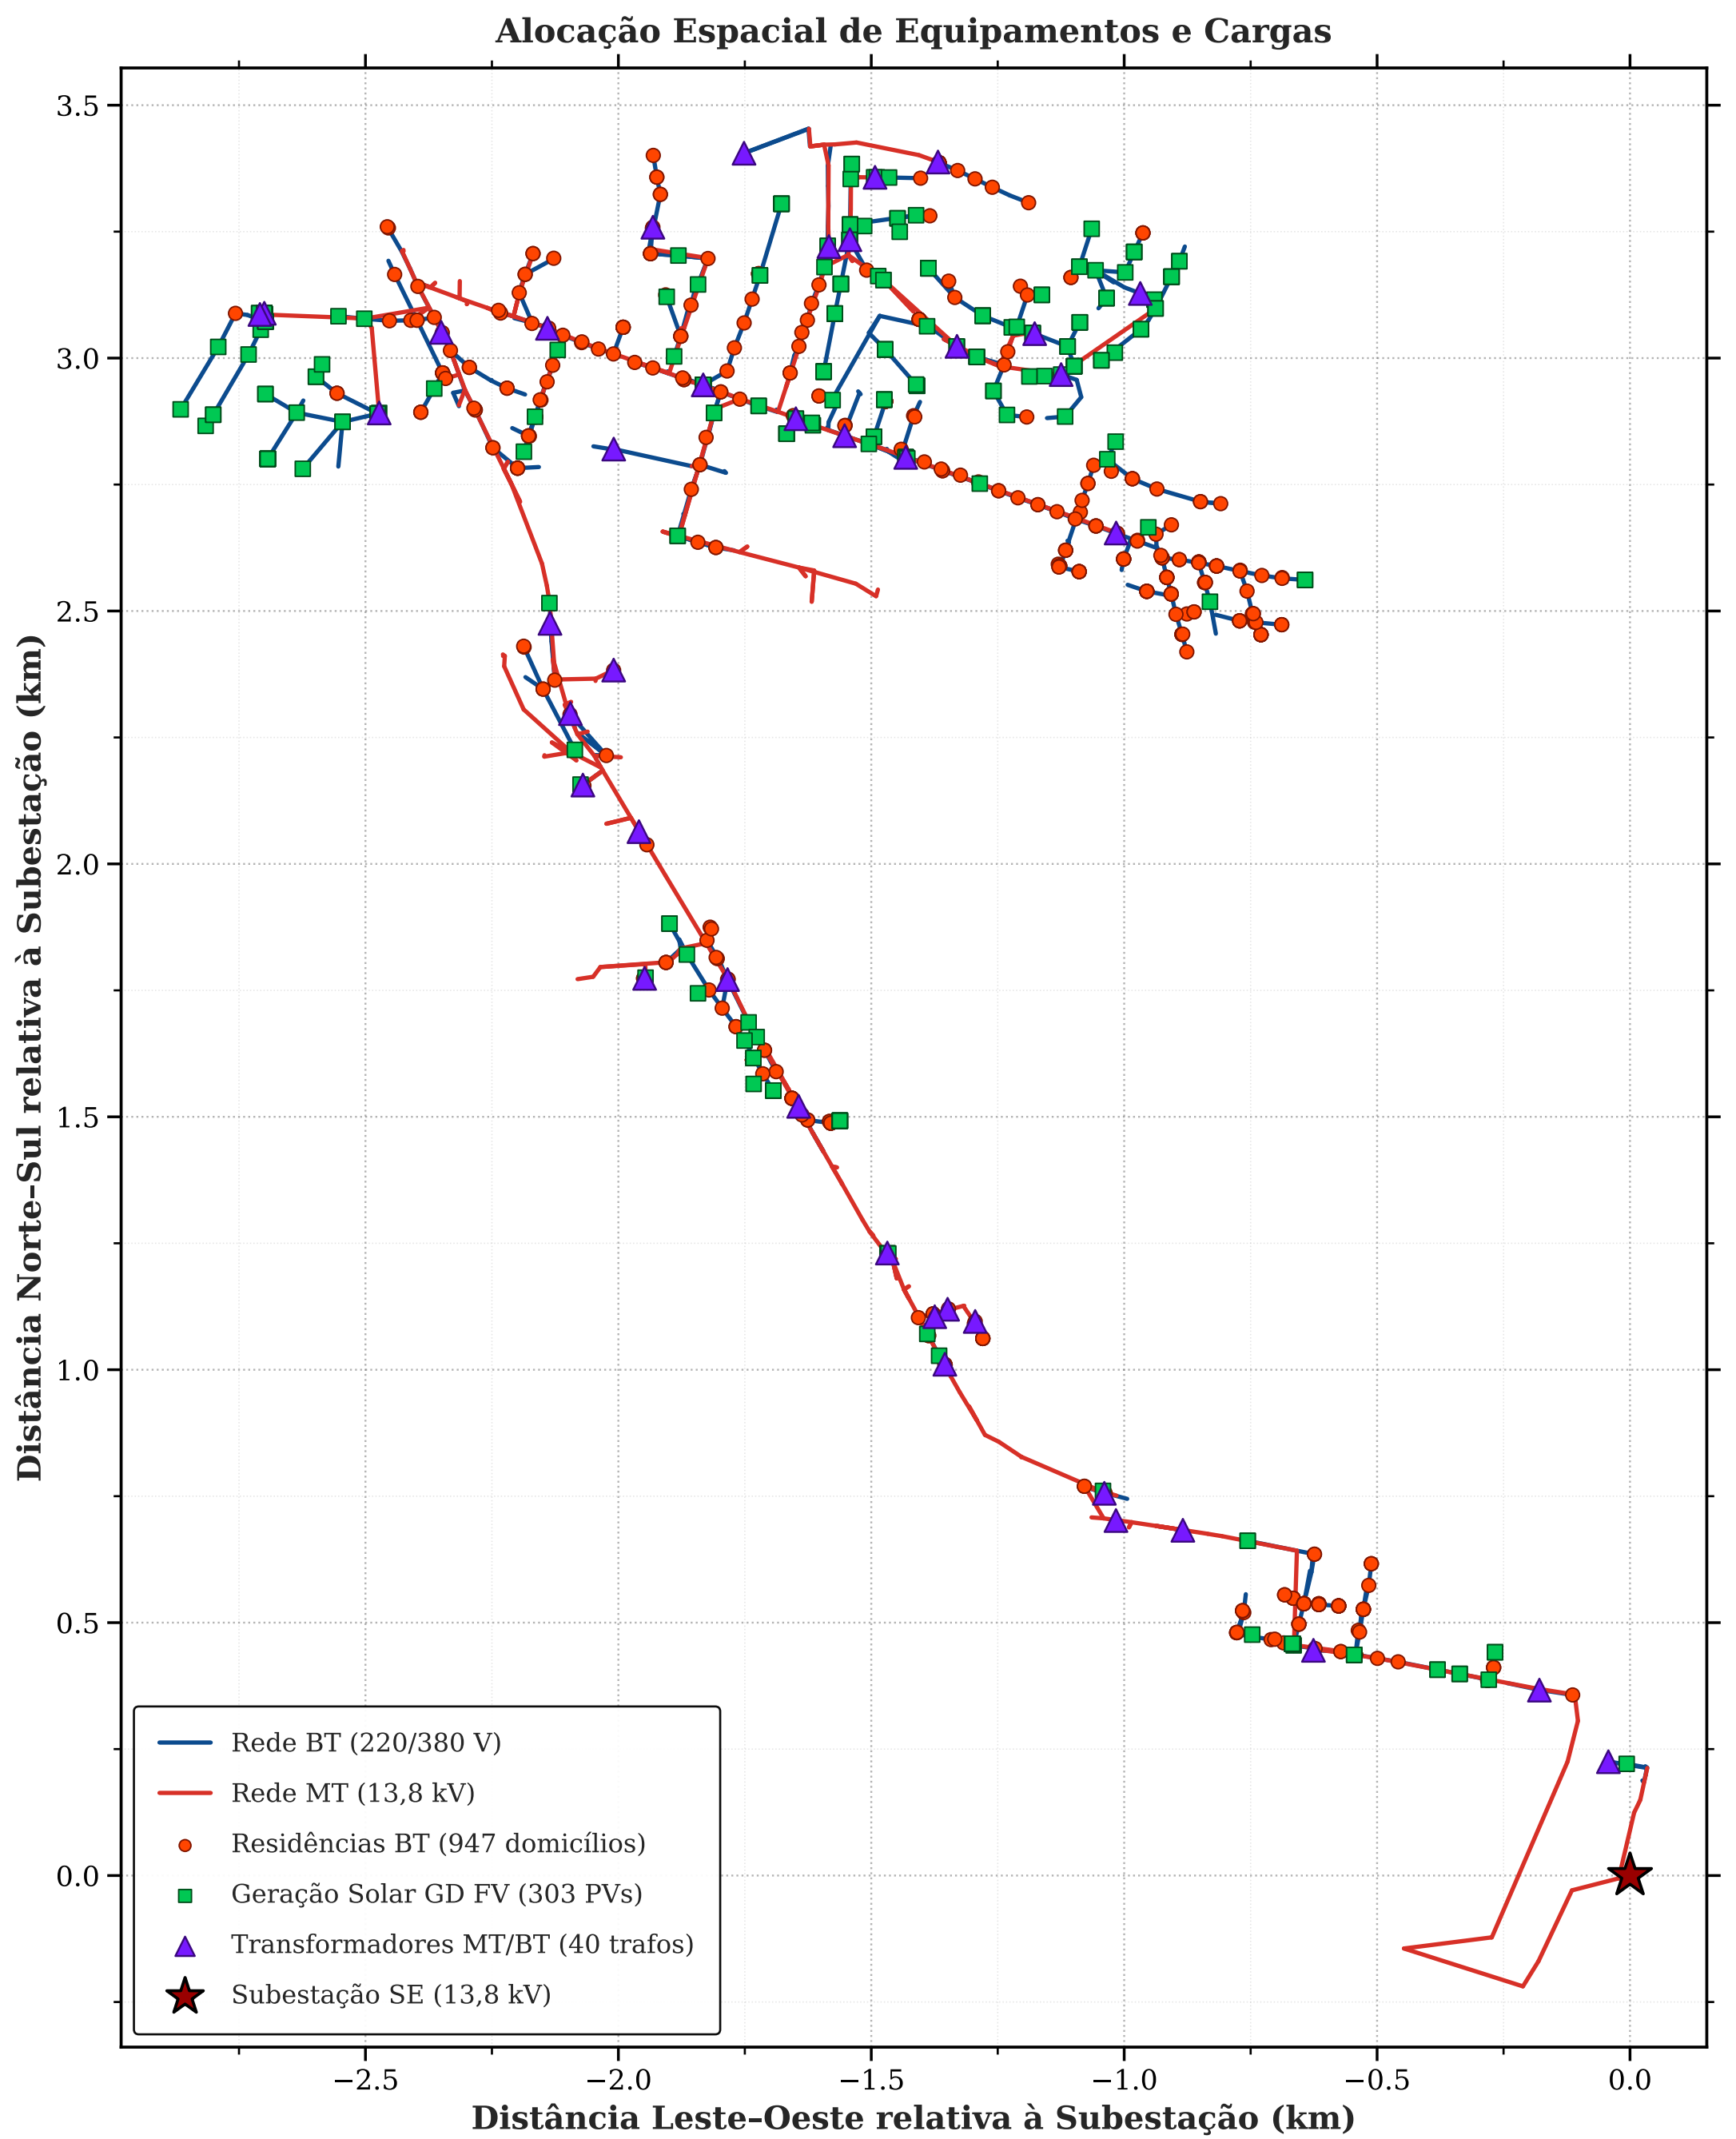

Alocação Espacial de Equipamentos e Cargas
Distância Norte-Sul relativa à Subestação (km)
3.5
3.0
2.5
2.0
1.5
1.0
0.5
0.0
−2.5
−2.0
−1.5
−1.0
−0.5
0.0
Distância Leste-Oeste relativa à Subestação (km)
Rede BT (220/380 V)
Rede MT (13,8 kV)
Residências BT (947 domicílios)
Geração Solar GD FV (303 PVs)
Transformadores MT/BT (40 trafos)
Subestação SE (13,8 kV)